

TEA HOUSE / VERIFIED CIRCULATION

102 room-to-stair routes · 0.80 m body width · 2.10 m headroom · measured on exported GLB at 5 cm grid spacing


G Tea House
12 standing zones reach both stairs · longest nearest-stair route 17.6 m

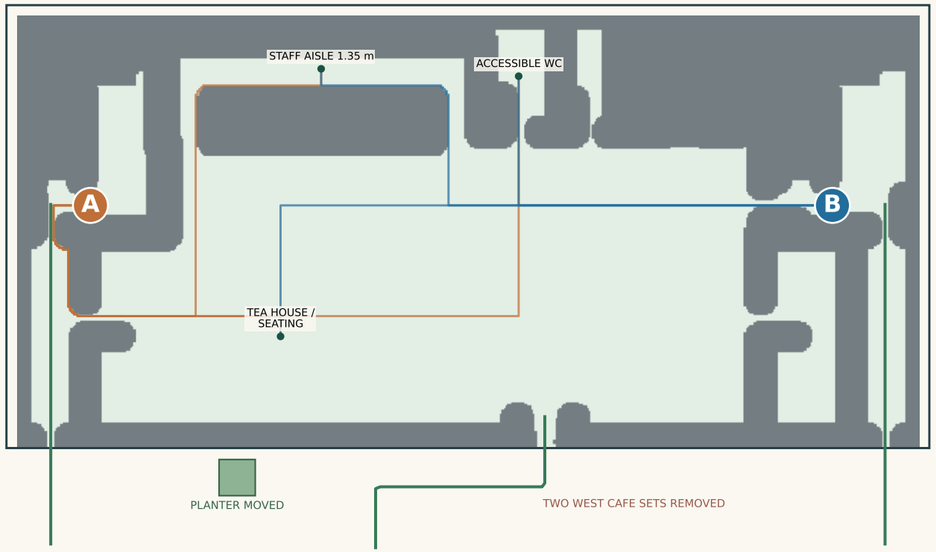


L1 Tea salon & community
9 standing zones reach both stairs · longest nearest-stair route 14.6 m

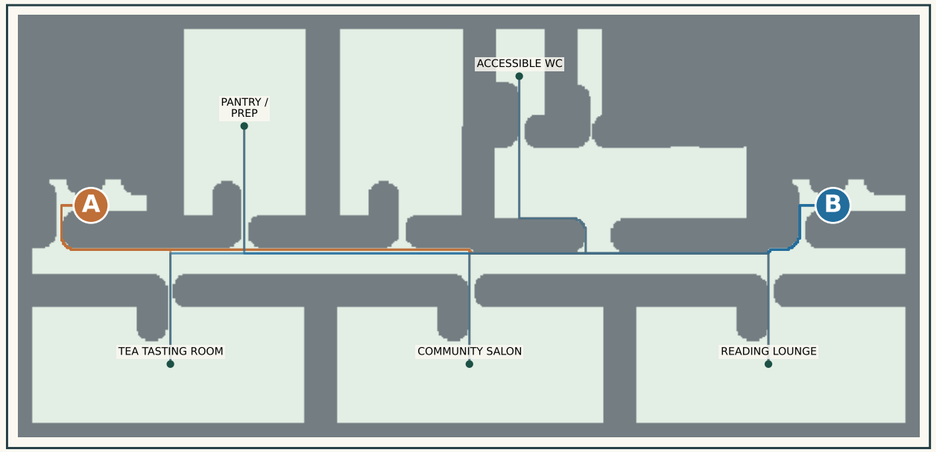

L2 Residences 201-203
15 standing zones reach both stairs · longest nearest-stair route 16.3 m

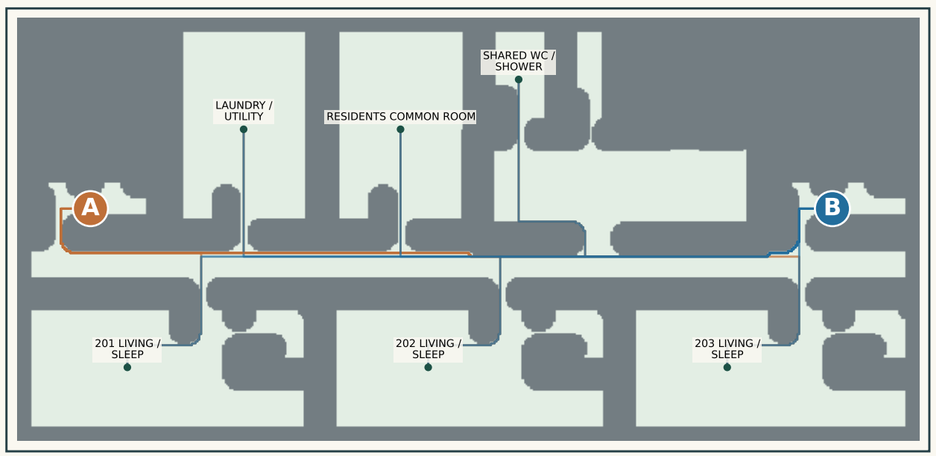


L3 Residences 301-303
15 standing zones reach both stairs · longest nearest-stair route 16.3 m

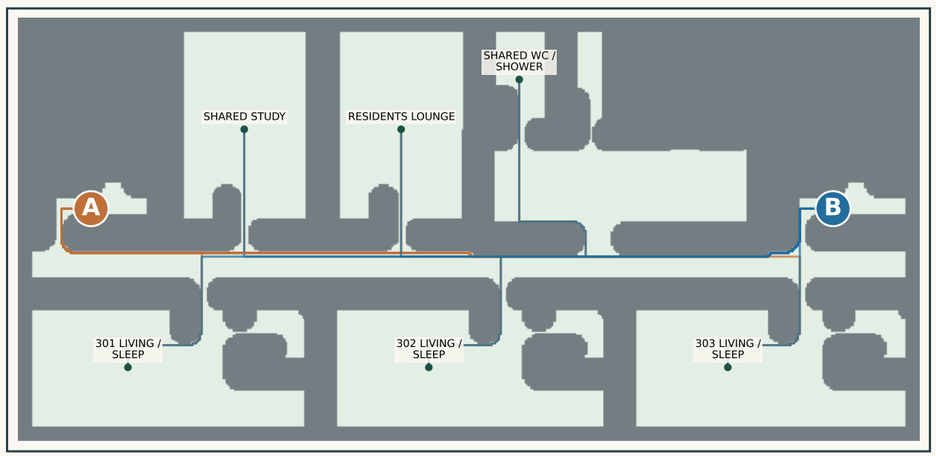


Green areas = valid body centres; gray = clearance excluded. Orange routes → stair A; blue routes → stair B. Representative routes shown; all 102 checked.
Exterior traces include the required cafe removals and planter relocation. Private rooms are intentional single-entry destinations. This is a structure audit, not live navigation.


G Tea House
12 standing zones reach both stairs · longest nearest-stair route 17.6 m

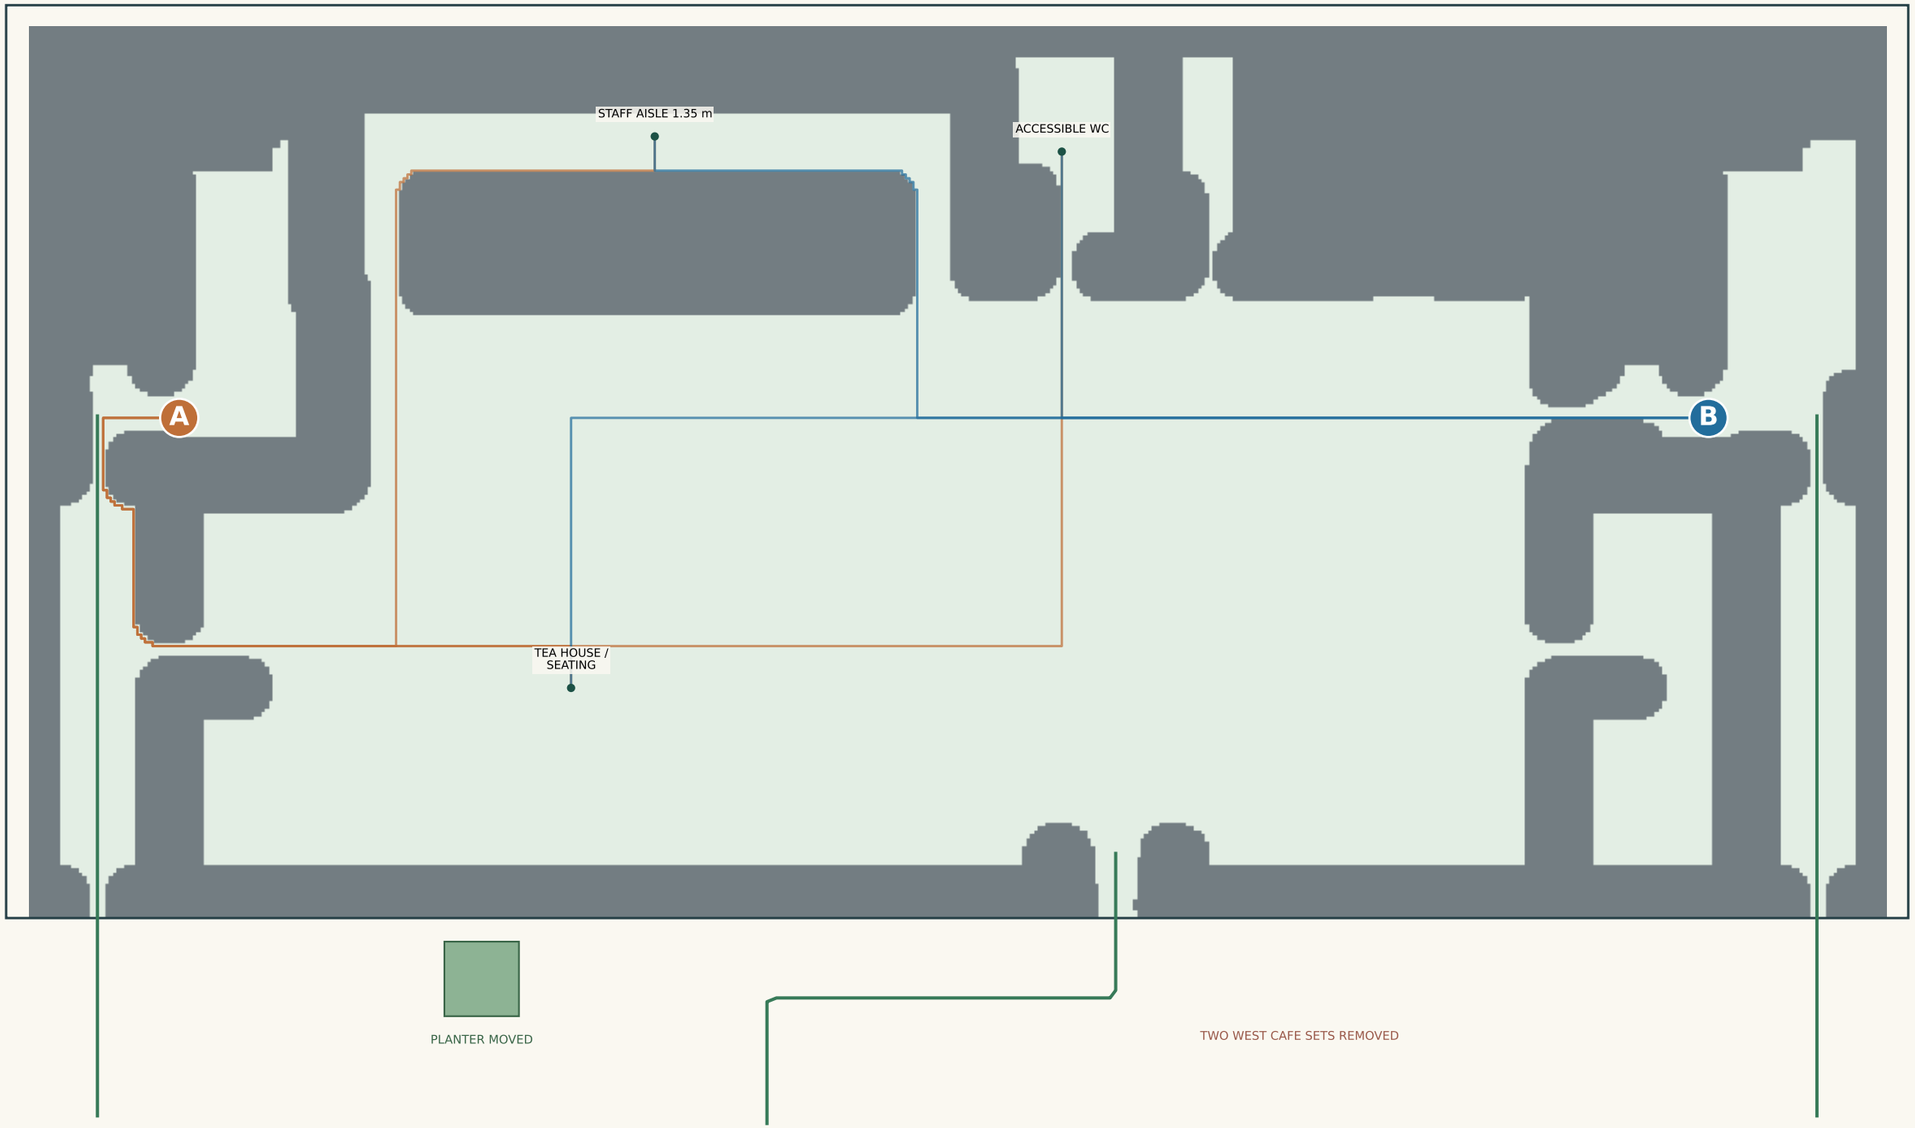

L1 Tea salon & community
9 standing zones reach both stairs · longest nearest-stair route 14.6 m

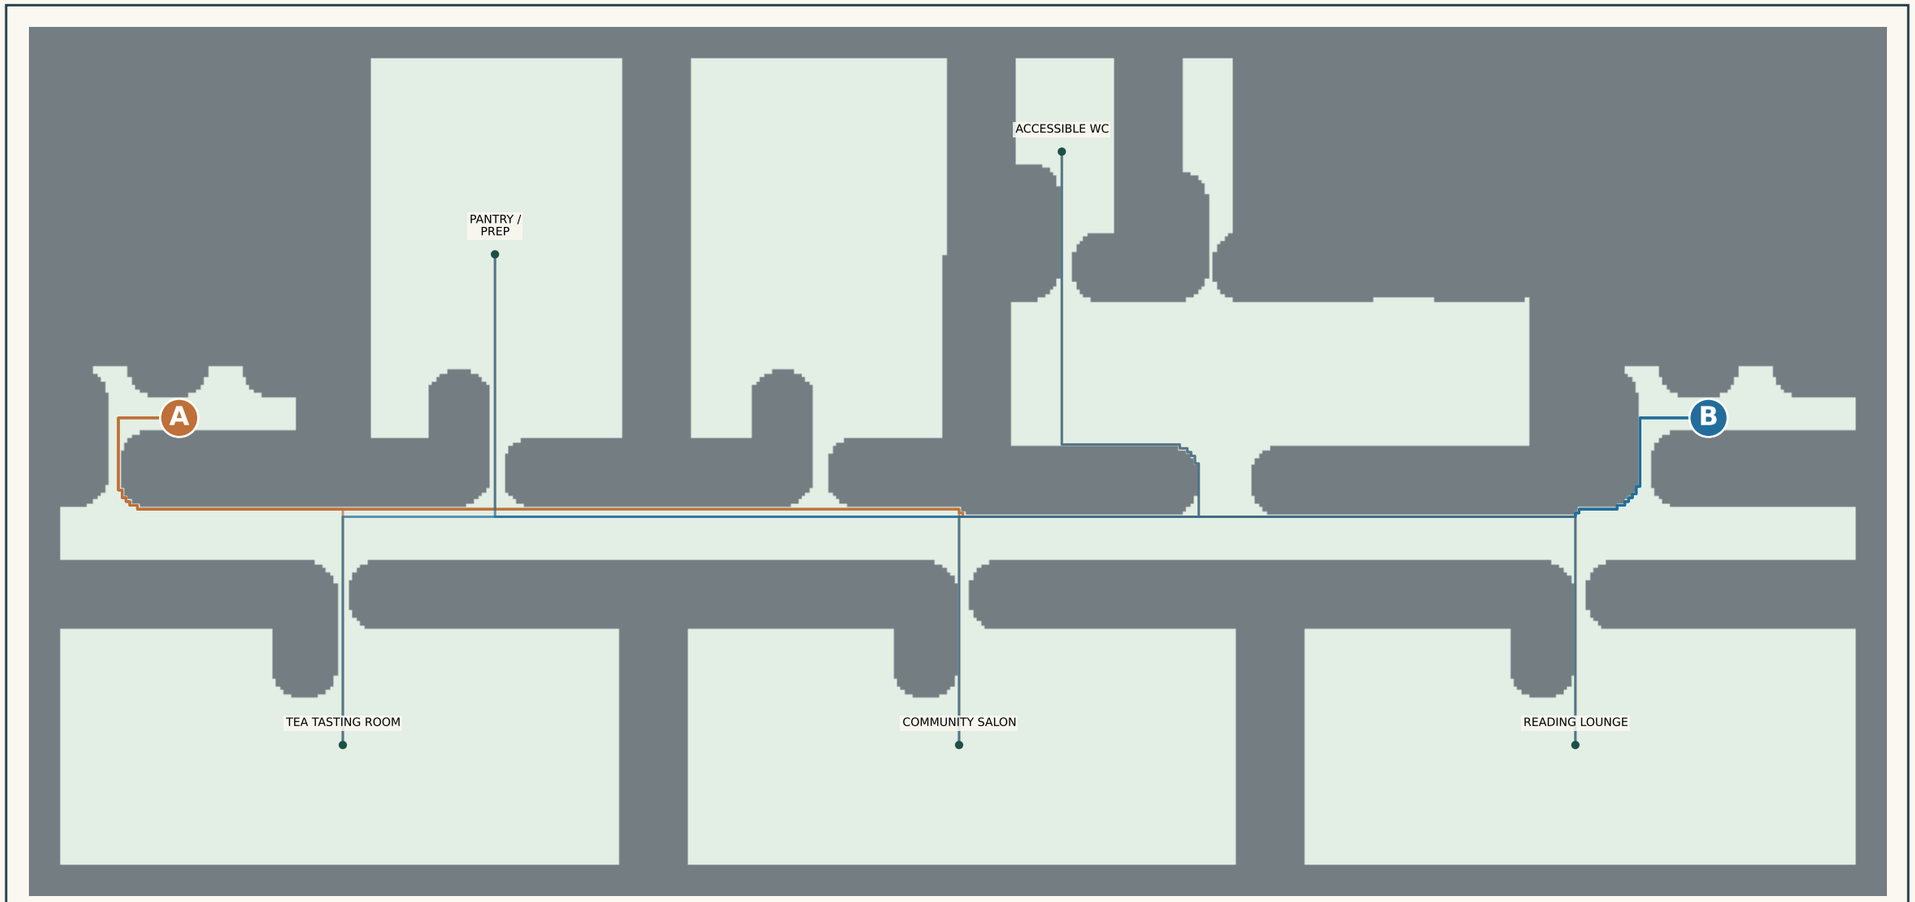

L2 Residences 201-203
15 standing zones reach both stairs · longest nearest-stair route 16.3 m

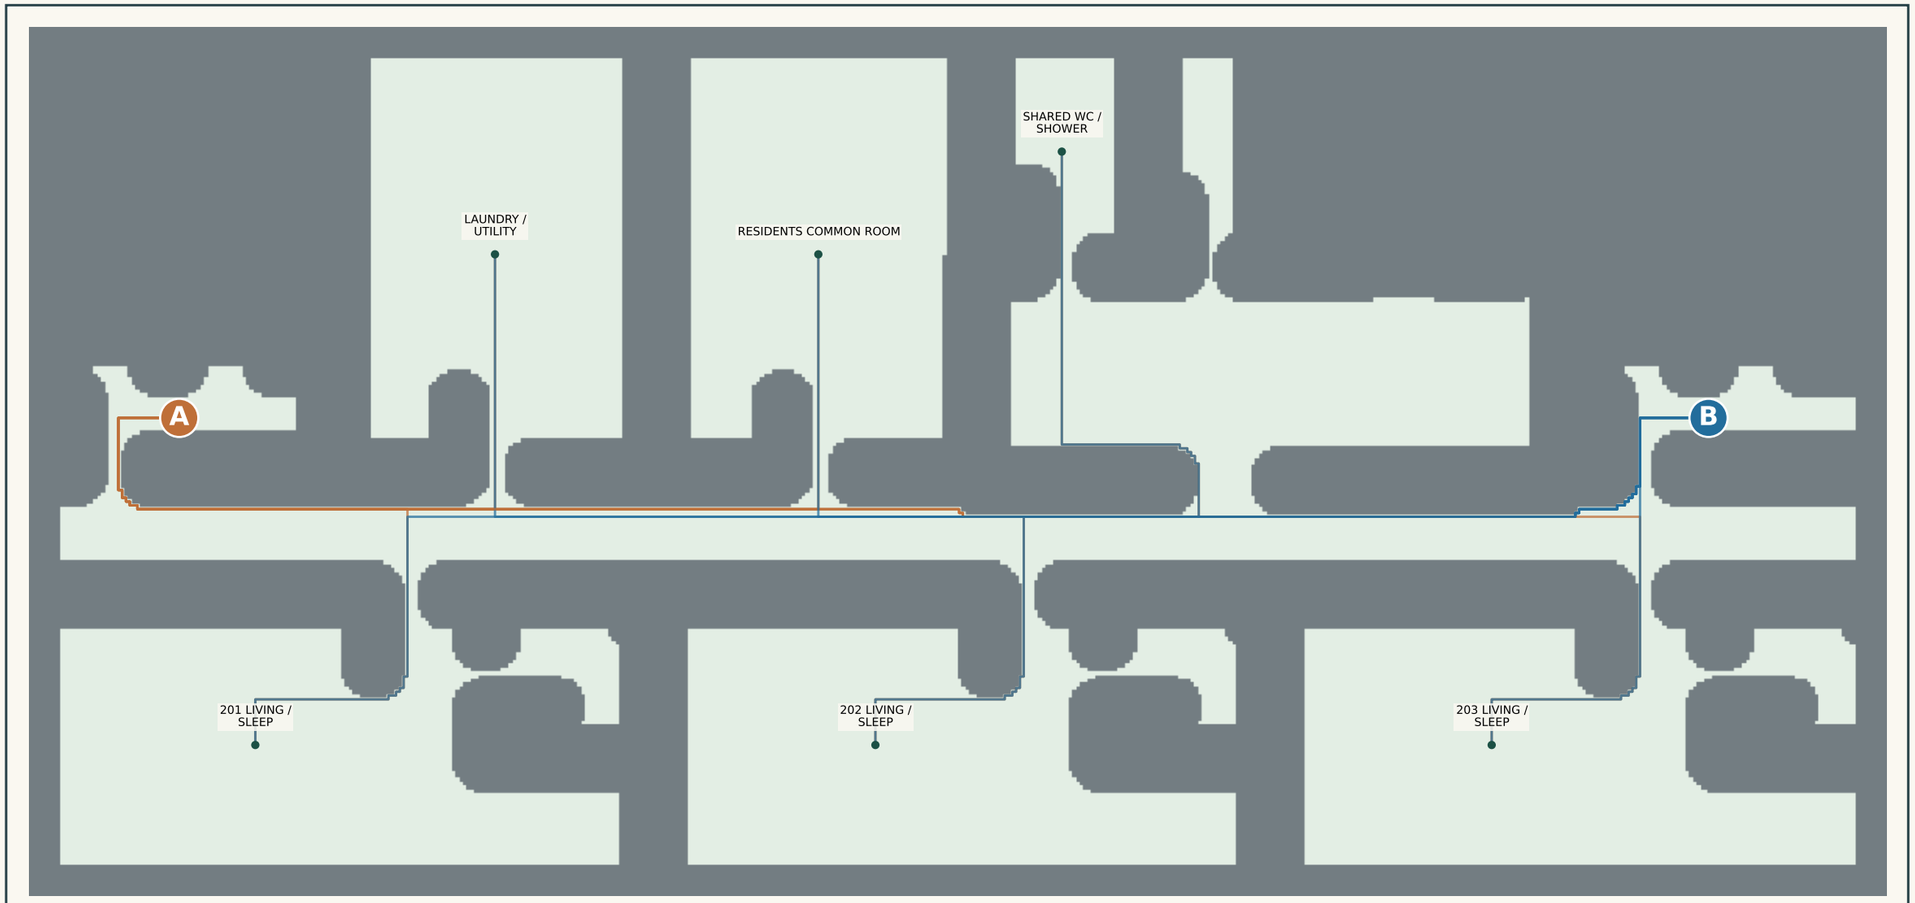

L3 Residences 301-303
15 standing zones reach both stairs · longest nearest-stair route 16.3 m

